



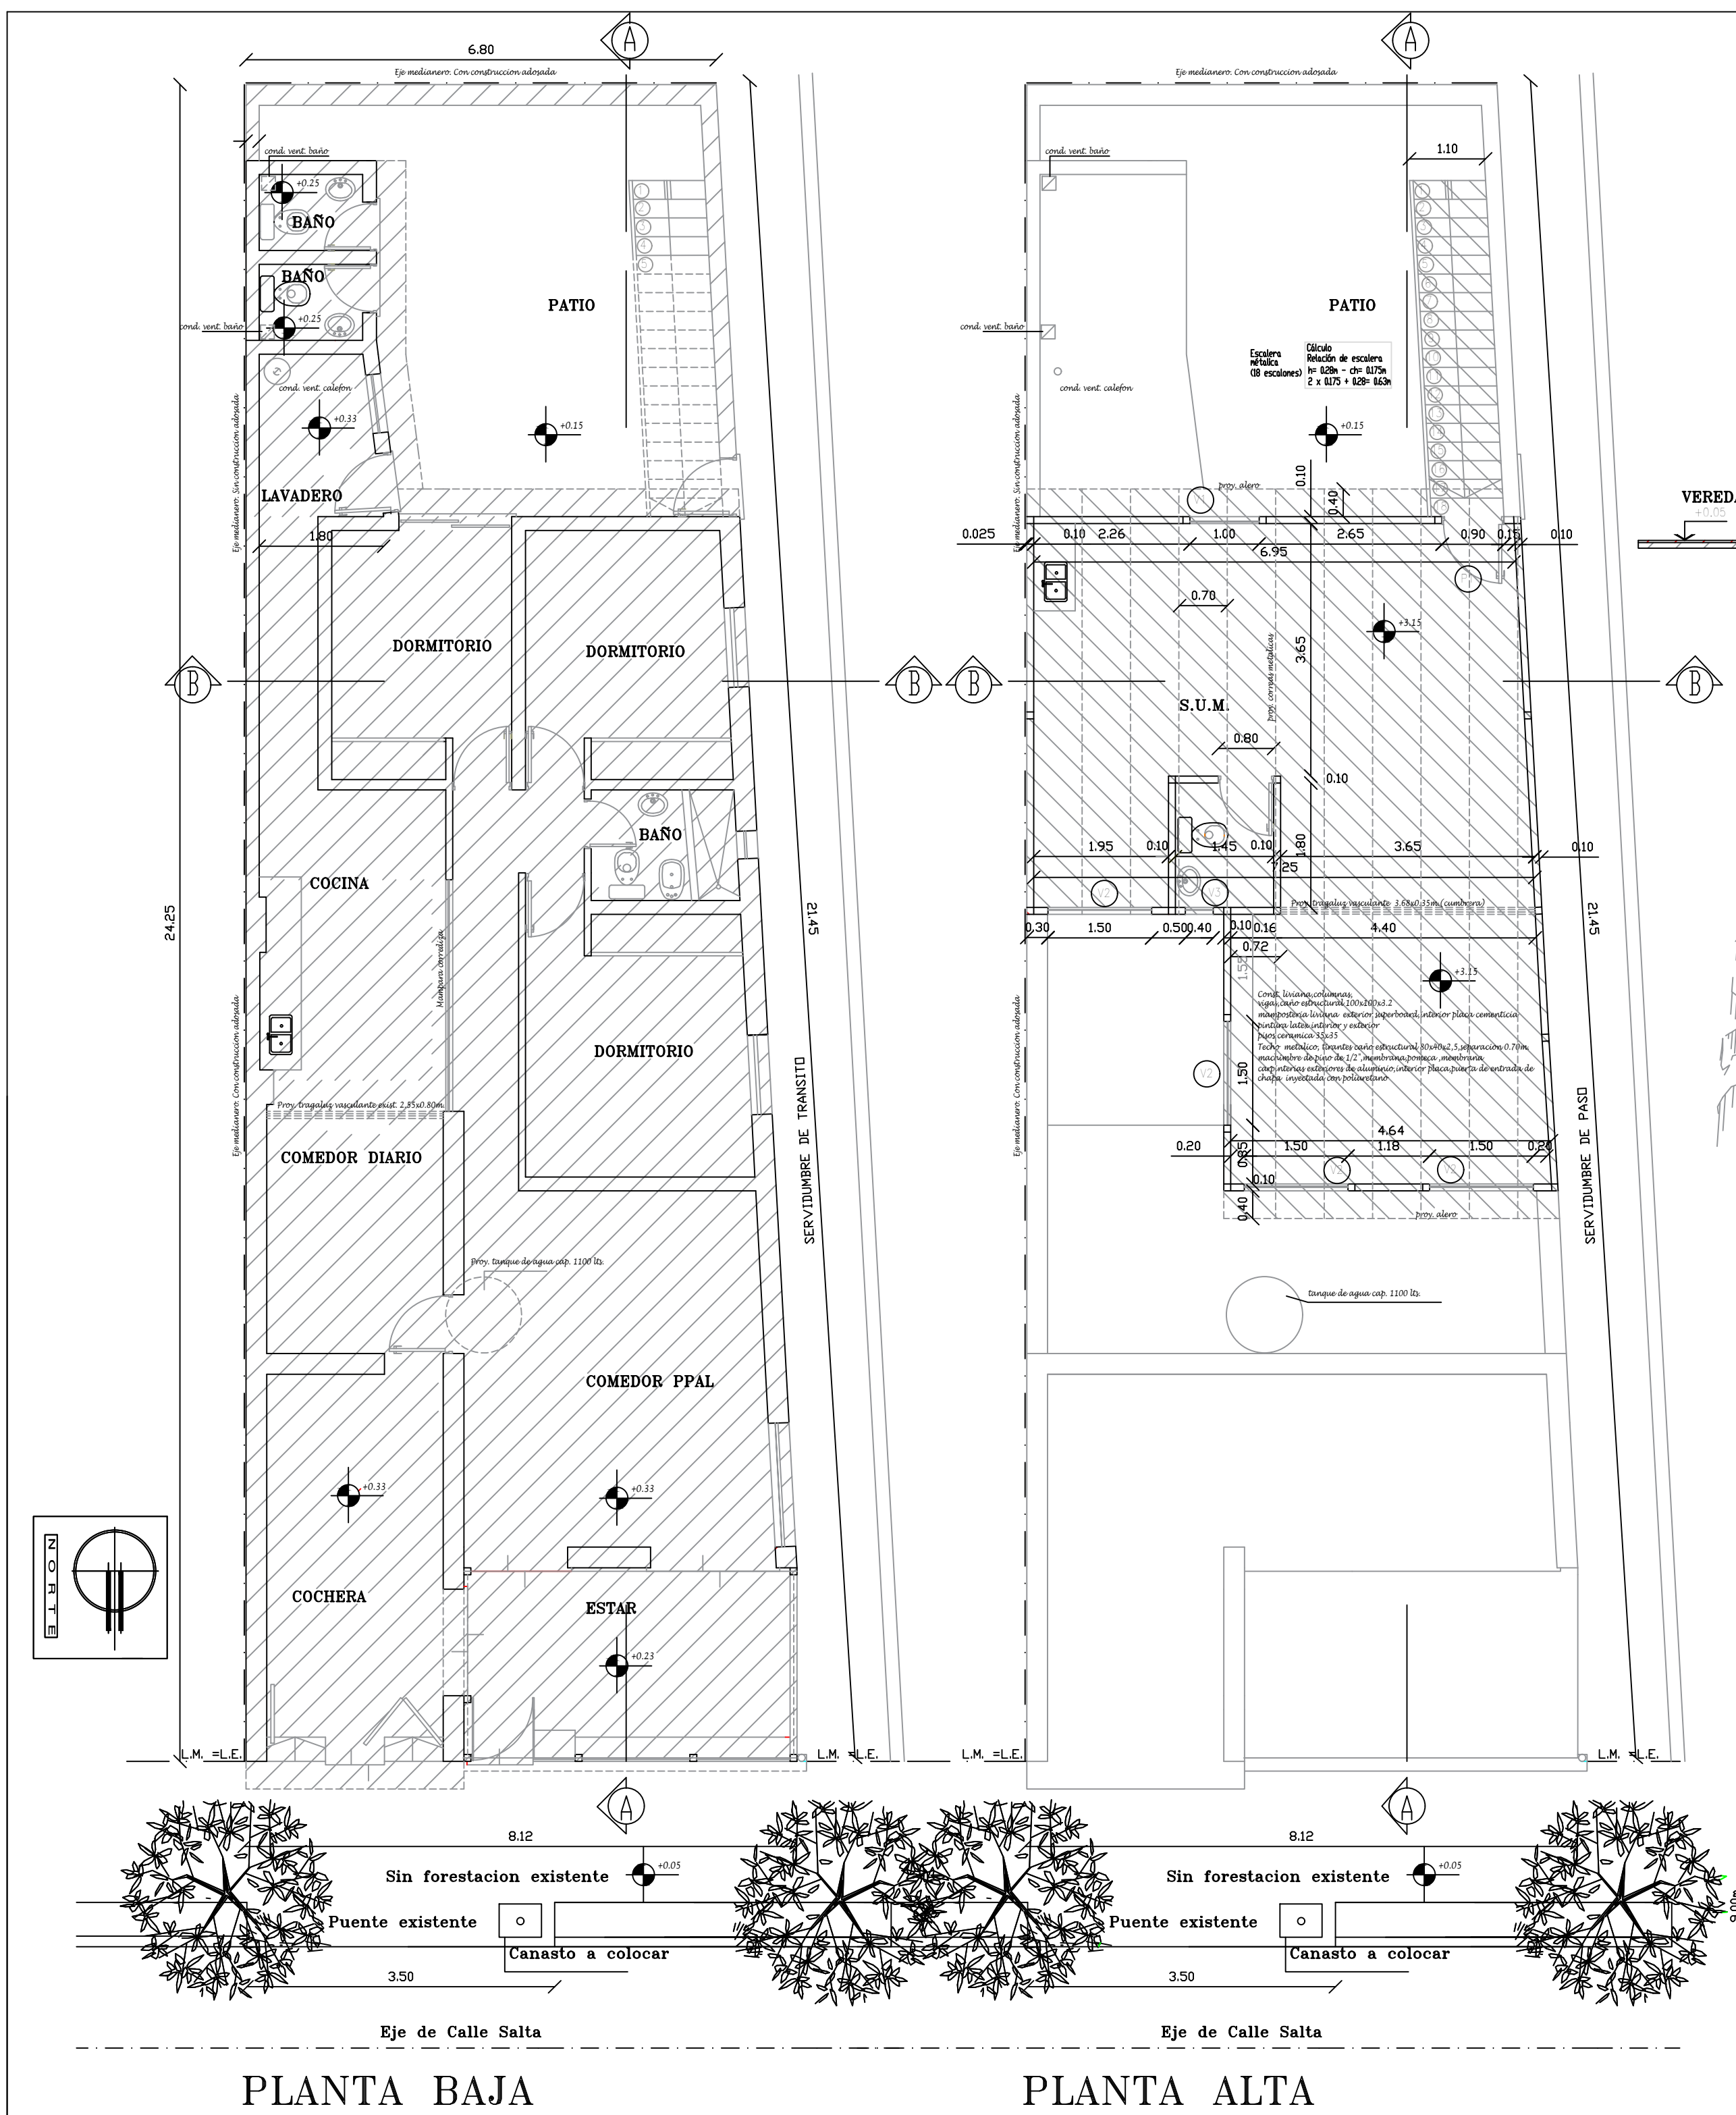


CORTE A-A

REFERENCIAS:
SUPERFICIE CUBIERTA EXISTENTE S/EXPT.E.N°53946/E/11
SUPERFICIE CUBIERTA EXISTENTE A DECLARAR

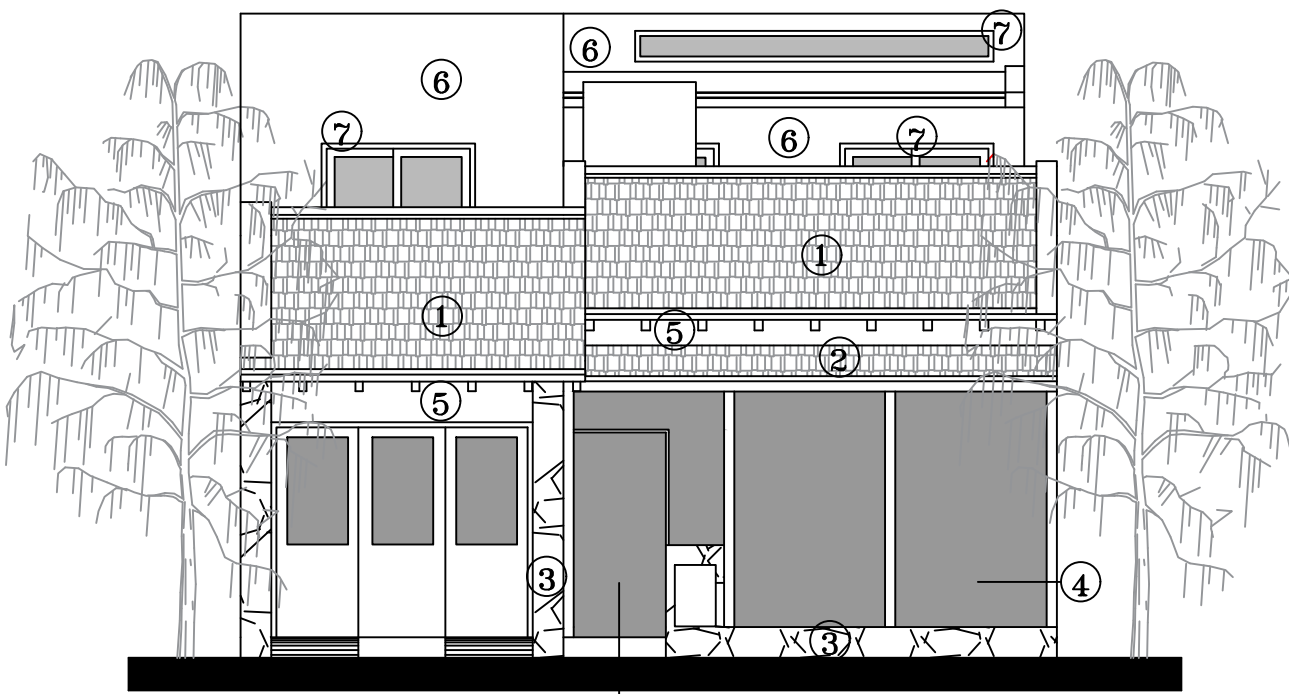

FACHADA

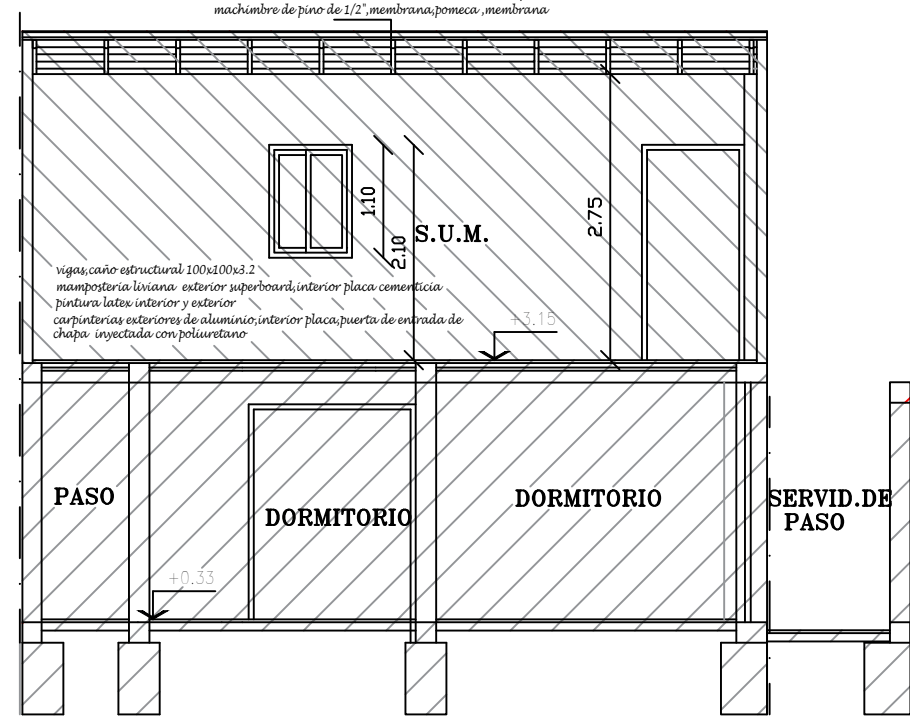

CORTE B-B


- REFERENCIAS FACHADA:
- 1 TEJA COLONIAL
 - 2 TEJA PORTUGUESA
 - 3 PIEDRA
 - 4 VIDRIO DE SEGURIDAD
 - 5 REVOQUE GRUESO Y FINO PINTADO
 - 6 REVESTIMIENTO PLASTICO
 - 7 CARPINTERIA DE ALUMINIO

PLANILLA ILUMINACION - VENTILACION

N°	LOCAL	SUPERF. m2	ABERTURAS	% ILUMIN.	% VENTIL.	RESERV.
			TIPO	ANCHO	ALTO	
			m.	m.	m.	
PLANTA ALTA						
1	S.U.M.	57.62	1.00 x 1.50	1.00 x 1.50	1.00	1.00
2	BAÑO	3.24	1.00 x 1.50	1.00 x 1.50	1.00	1.00

PLANILLA DE LOCALES

N°	LOCAL	CARPETA A*	PISOS	REVOQUES	REVESTIMIENTOS	CIELORRASOS	PINTURAS
		mater. espes. cm.	mater. dimens. cm.	grueso lino	mater. dimens. cm.	mater. termin.	MUROS CARPINT. CIELOR. tipomanos tipomanos tipomanos
PLANTA ALTA							
1	S.U.M.	H1P*	5 CERAM 30x30	9	9	—	MADERA APLICADO LATEX 2 ALUMINO — BARNIZ 2
2	BAÑO	H1P*	5 CERAM 30x30	9	14 CERAM 20x20	2.10	MADERA APLICADO LATEX 2 ALUMINO — BARNIZ 2

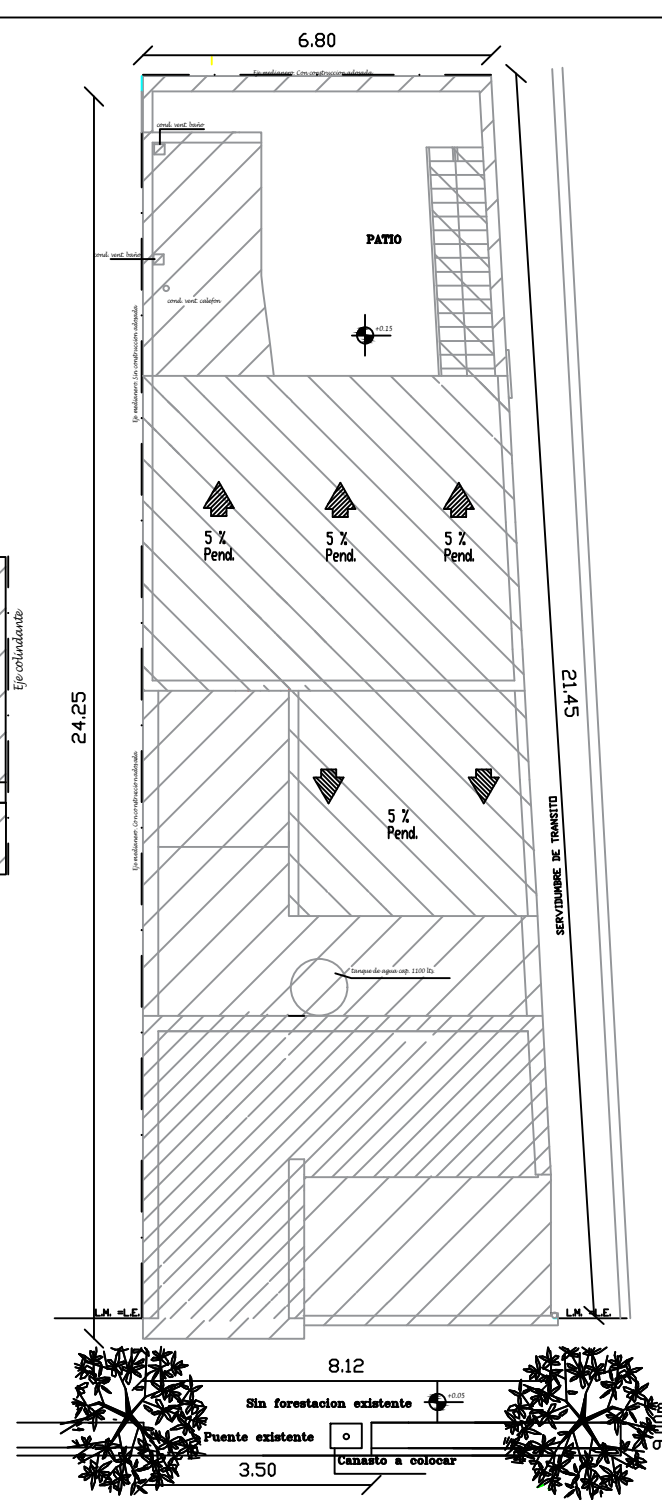

PLANTA DE TECHOS

PADRON MUNICIPAL N° 7387 NOM CATASTRAL 00-01-25-0007-000003-0000-0

OBRA: RELEVAMIENTO VIVIENDA
UBICACION: Salta 590- Godoy Cruz- Mza.
PROPIETARIO: LEONARDO A. SALINAS Y OTRA
DOMICILIO: Salta 590- Godoy Cruz- Mza.

Sup. Cub. Exist. s/inspección N° 5904/G/58 119.94 m2
Sup. Cub. Exist. s/inspección N° 4524/53 30.15 m2
Sup. Cub. Exist. s/inspección N° 53946/E/11 60.97 m2
Sup. Pisos: 31.58 m2
Sup. Terrazo: 188.77 m2
Sup. Cub. a declarar al 100% 215.74 m2

PLANO ARQUITECTURA ESC. 1:50 1

RELEVO: ESTERAN PATRIN - Arquitecto
MAT. 1912
Domicilio: Vinyes 2889- Mapa-Mercaderes

CROQUIS DE UBICACION:
VIVIENDA
CALLE
CALLE

VISACION PREVIA SUBS.:
APROBACION: